

Jing-Zhang Standing for People


Human-Centered Urban Design for the Centennial Jing-Zhang AI Innovation Belt

Overall design area about 11.4 km2; three key areas about 3.68 km2. Auditable design deliverable.

1. Concept: Human-Centered, Ground Stitching

Jing-Zhang Standing for People returns the century-old railway heritage to the people who live, work and create here.

Jing-Zhang Standing for People - Centennial Jing-Zhang AI Innovation Belt, Overview (v1.14)

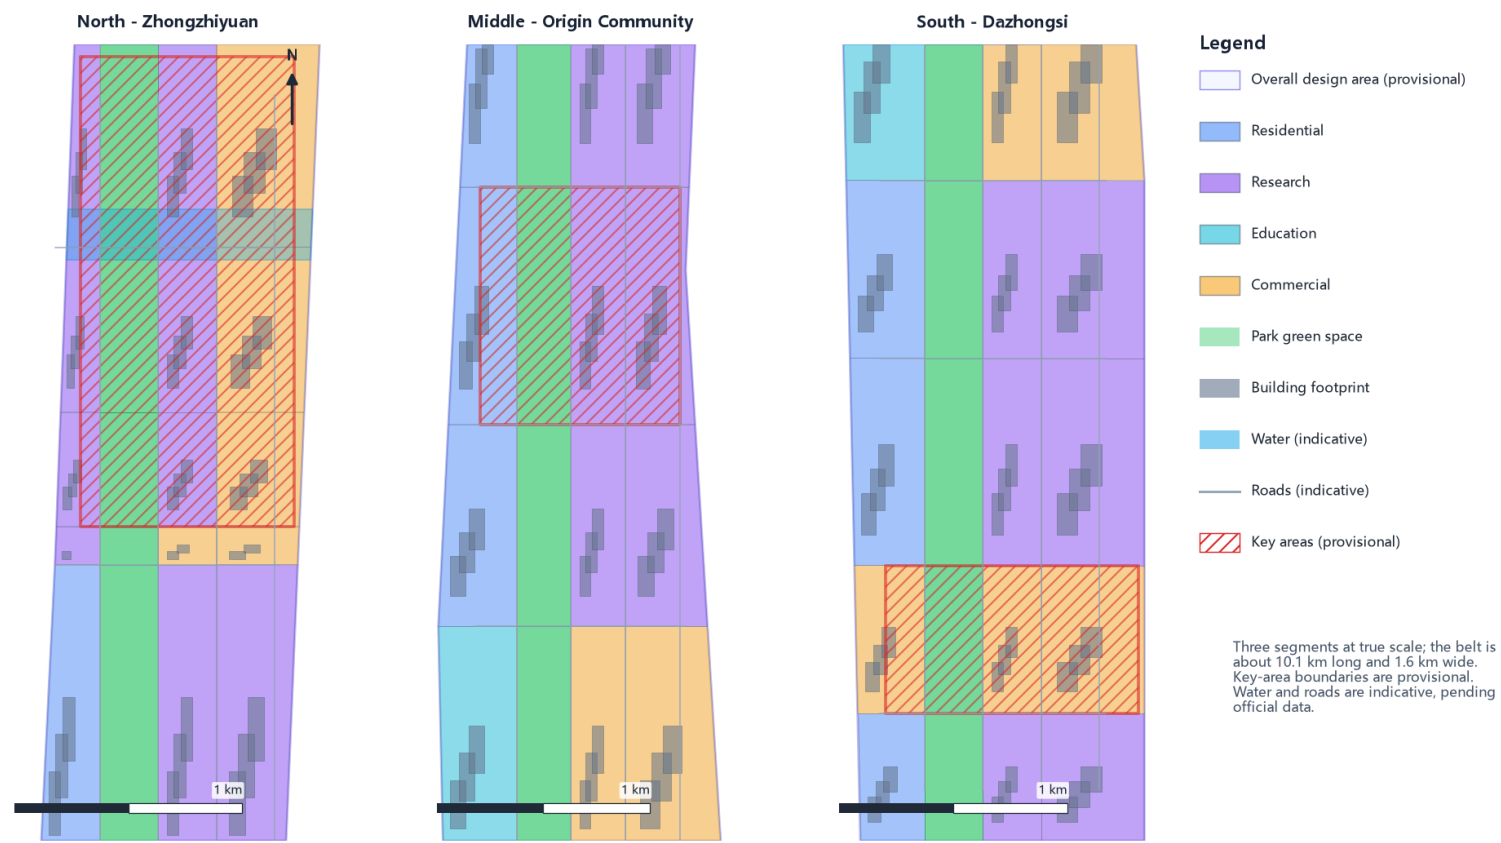

Legend and notes in the right-hand panel; design study under provisional boundaries - v1.14

Fig 1 Overview (provisional)

2. Land Use Structure and Functions

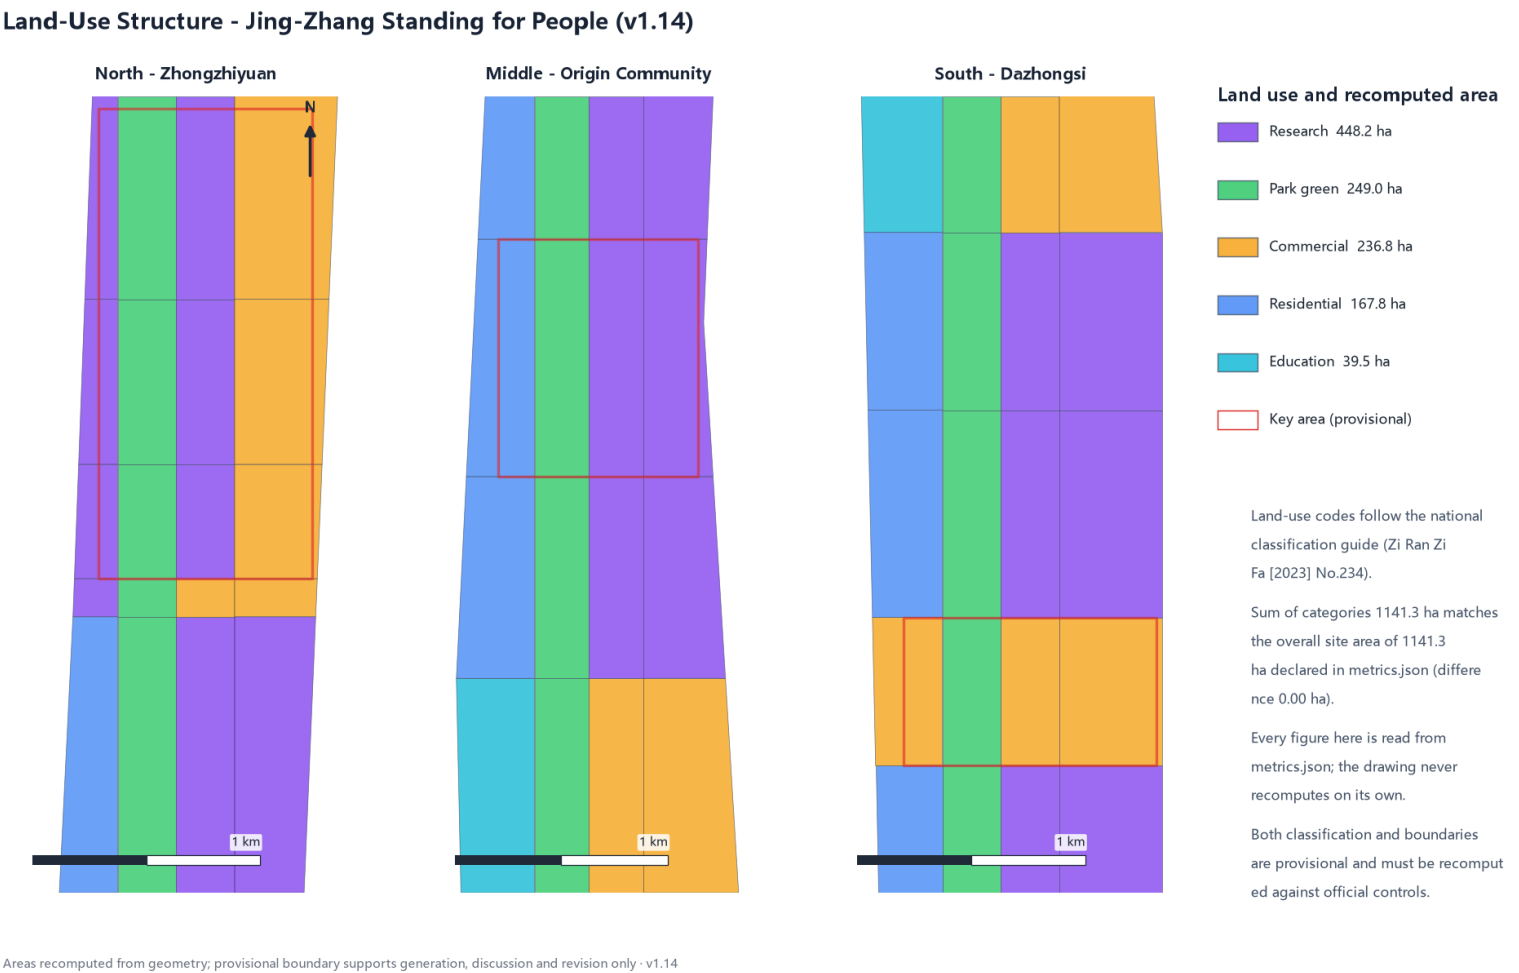


Fig 2 Land-use structure

3. Detailed Design of Three Key Areas

Location and Extent of the Three Key Areas (v1.14)


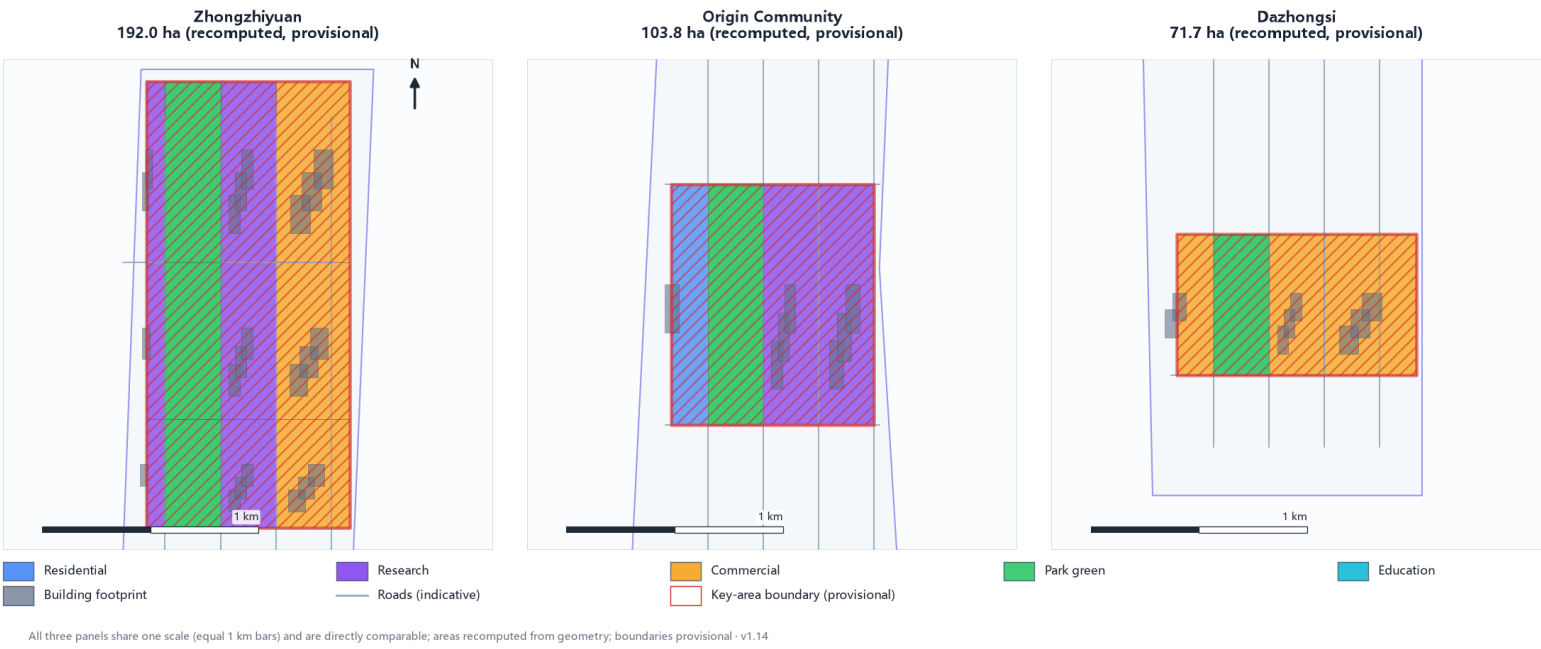


Fig 3 Three key areas

4. Transport, Slow Mobility and Blue-Green Space

Transport, Slow Mobility and Blue-Green Public Space (v1.14)

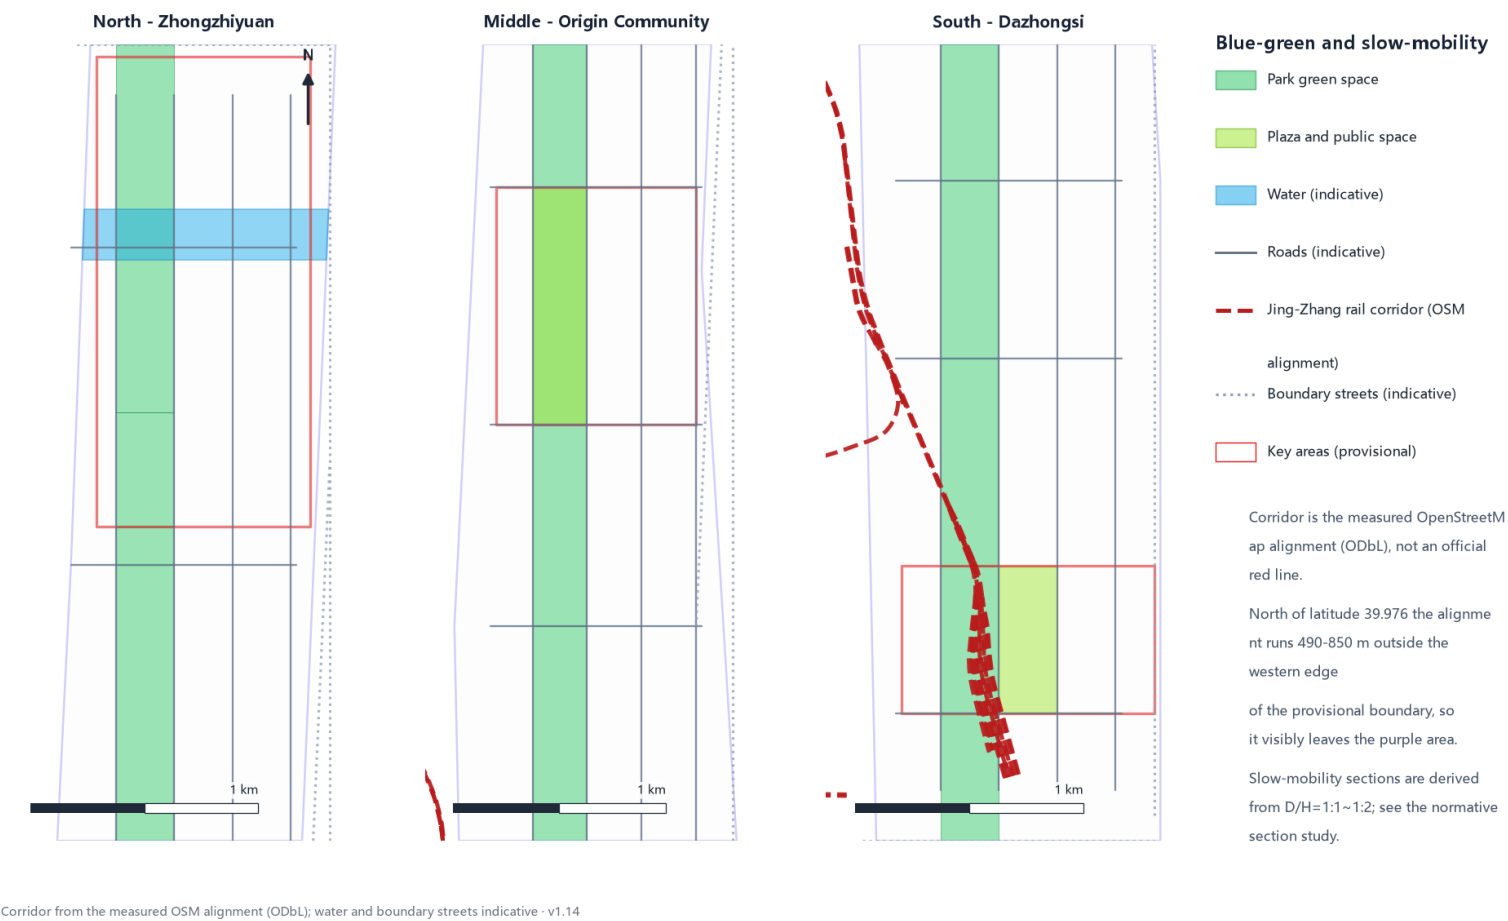

Corridor from the measured OSM alignment (ODbL); water and boundary streets indicative - v1.14

Fig 4 Transport and blue-green

6. Placement of the 12 AI Scenario Cards

Physical Placement of the 12 AI Scenario Cards - One Belt, Three Cores (v1.14)

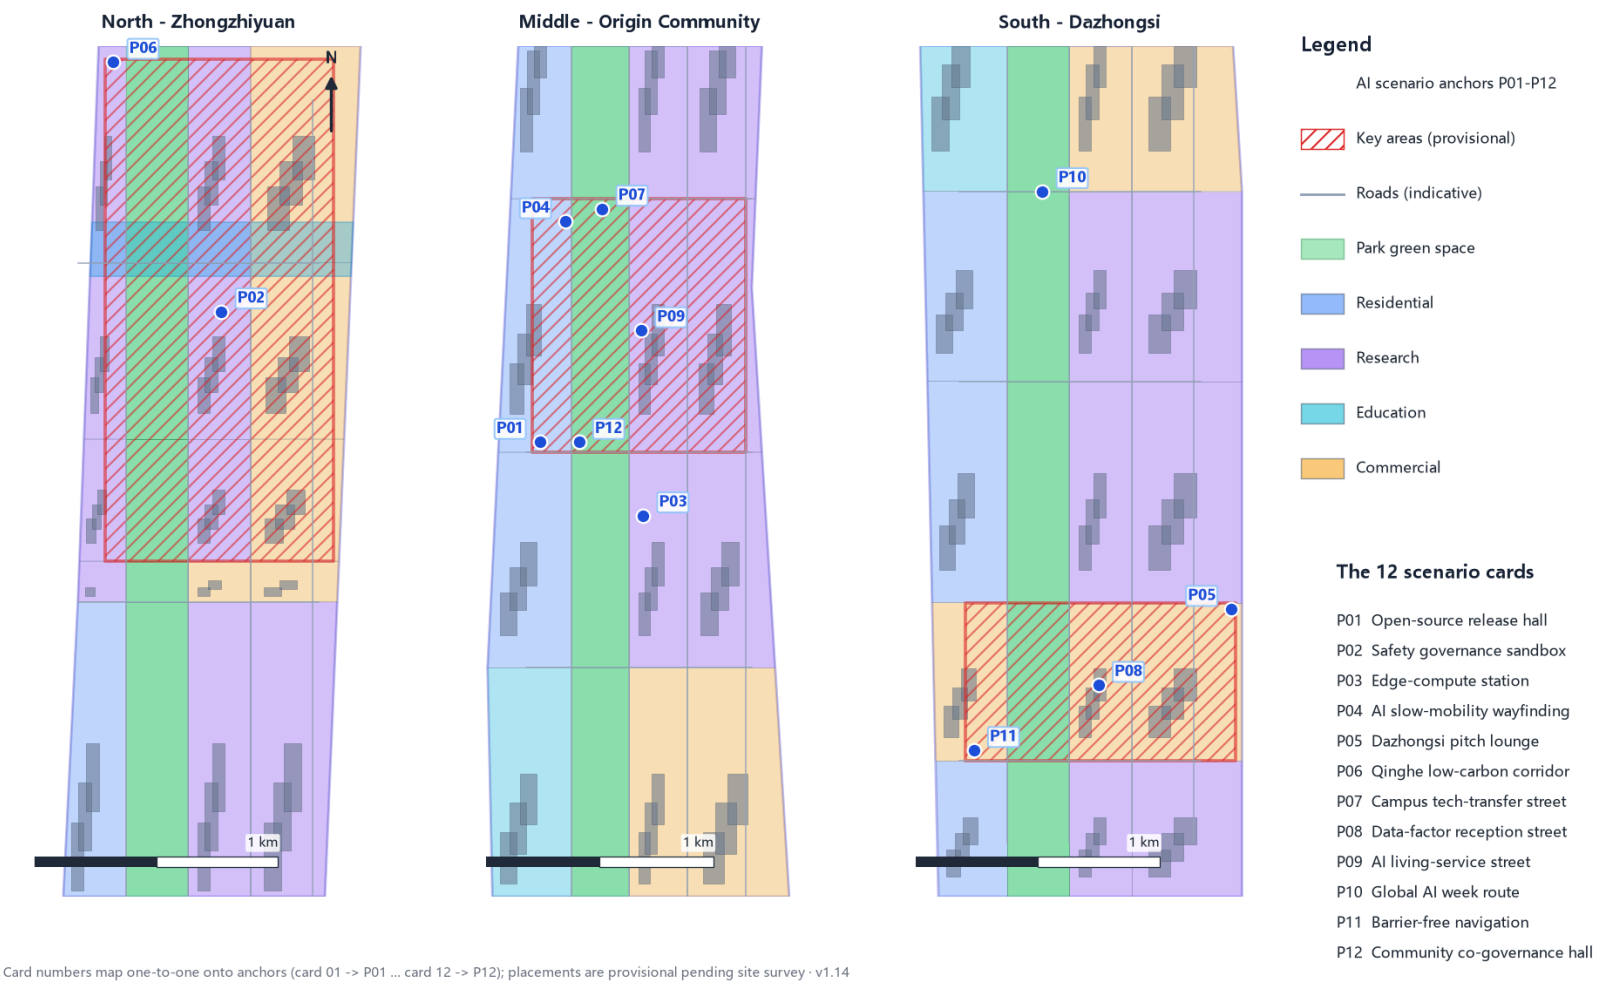


Fig 6 Physical placement of the 12 AI scenario cards

7. Spatial Deepening of the Key Areas

Spatial Deepening of the Key Areas - Site Anchors and AI Scenario Placement (v1.14)

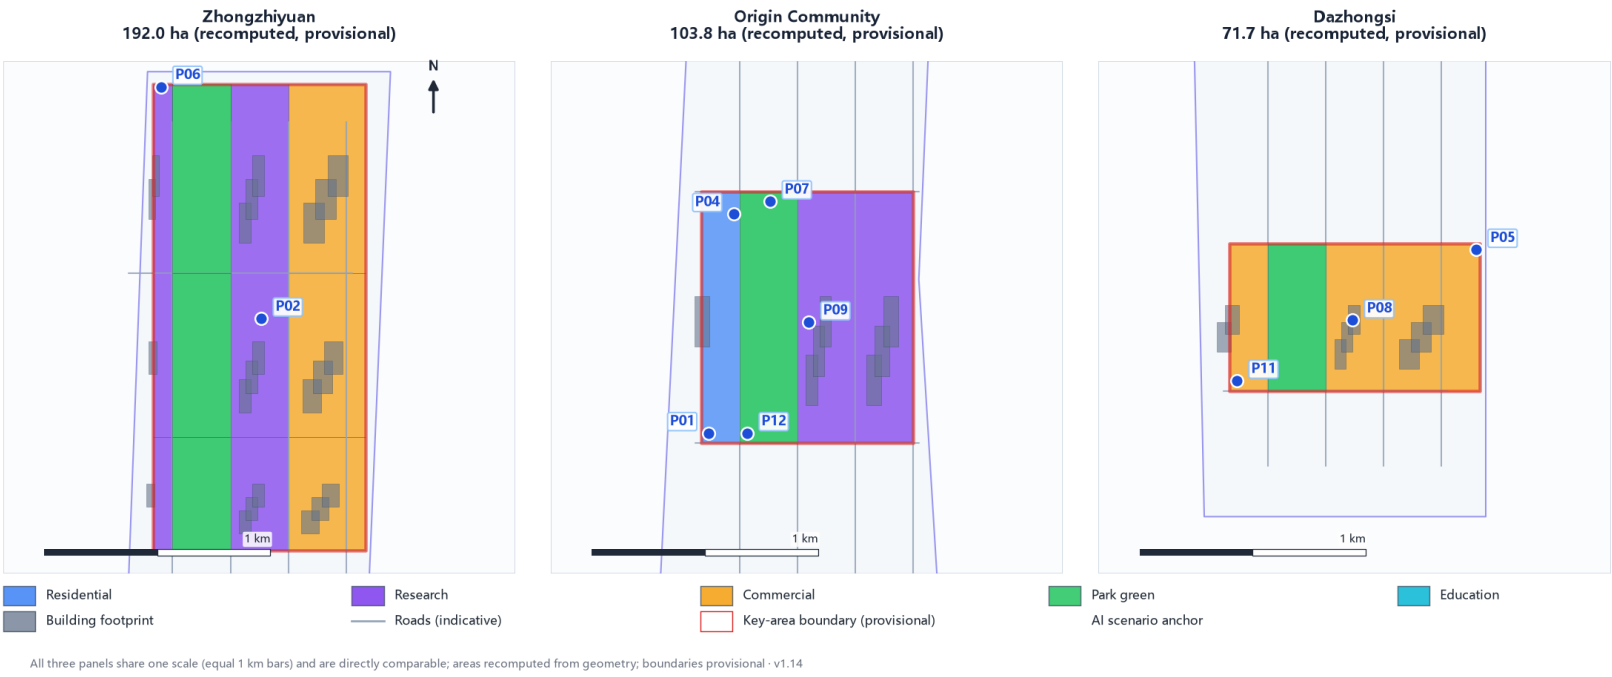


Fig 7 Site anchors and scenario placement in the key areas

8. Normative Street Sections (not measured)

Normative Street-Section Study - street width derived from the adopted D/H standard (not measured) (v1.13)

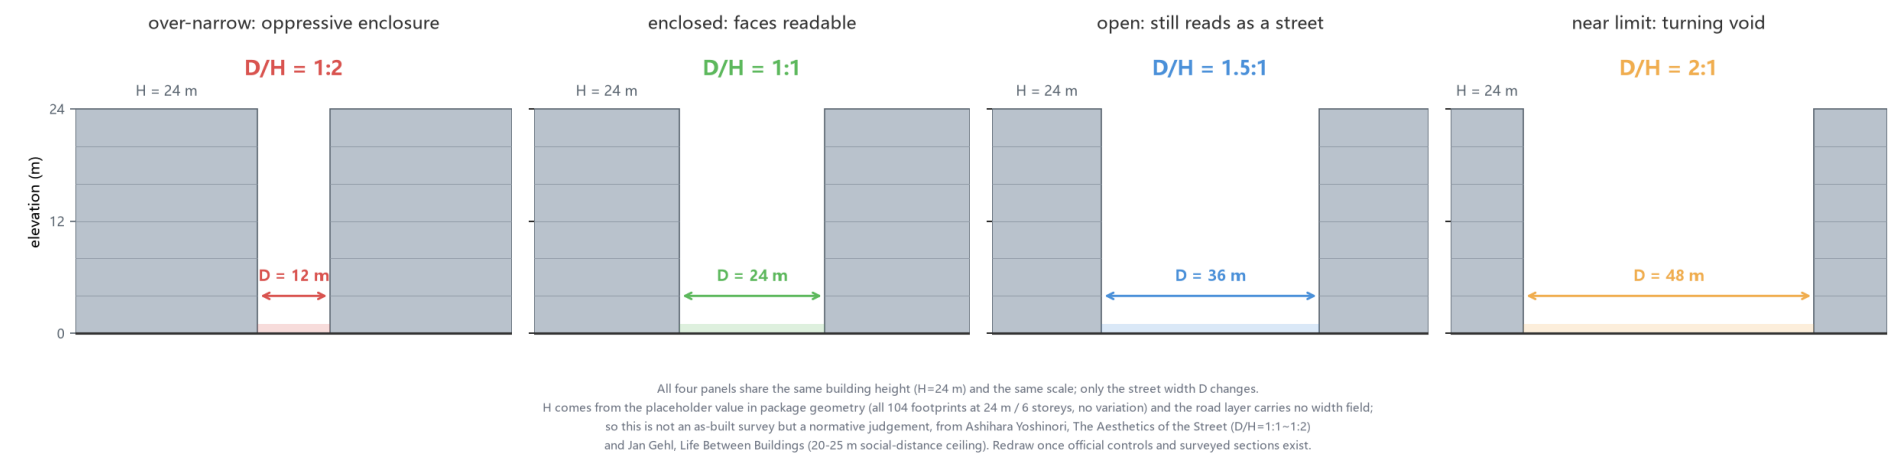


Fig 8 Normative sections: widths derived from D/H=1:1~1:2 and the 20-25 m social distance; building height uses the placeholder 24 m in package geometry, not a surveyed cross-section

5. Core Metric Recalculation

