



Jing-Zhang Standing for People – Exhibition Boards

Centennial Jing-Zhang AI Innovation Belt


Jing-Zhang Standing for People - Centennial Jing-Zhang AI Innovation Belt, Overview (v1.12)

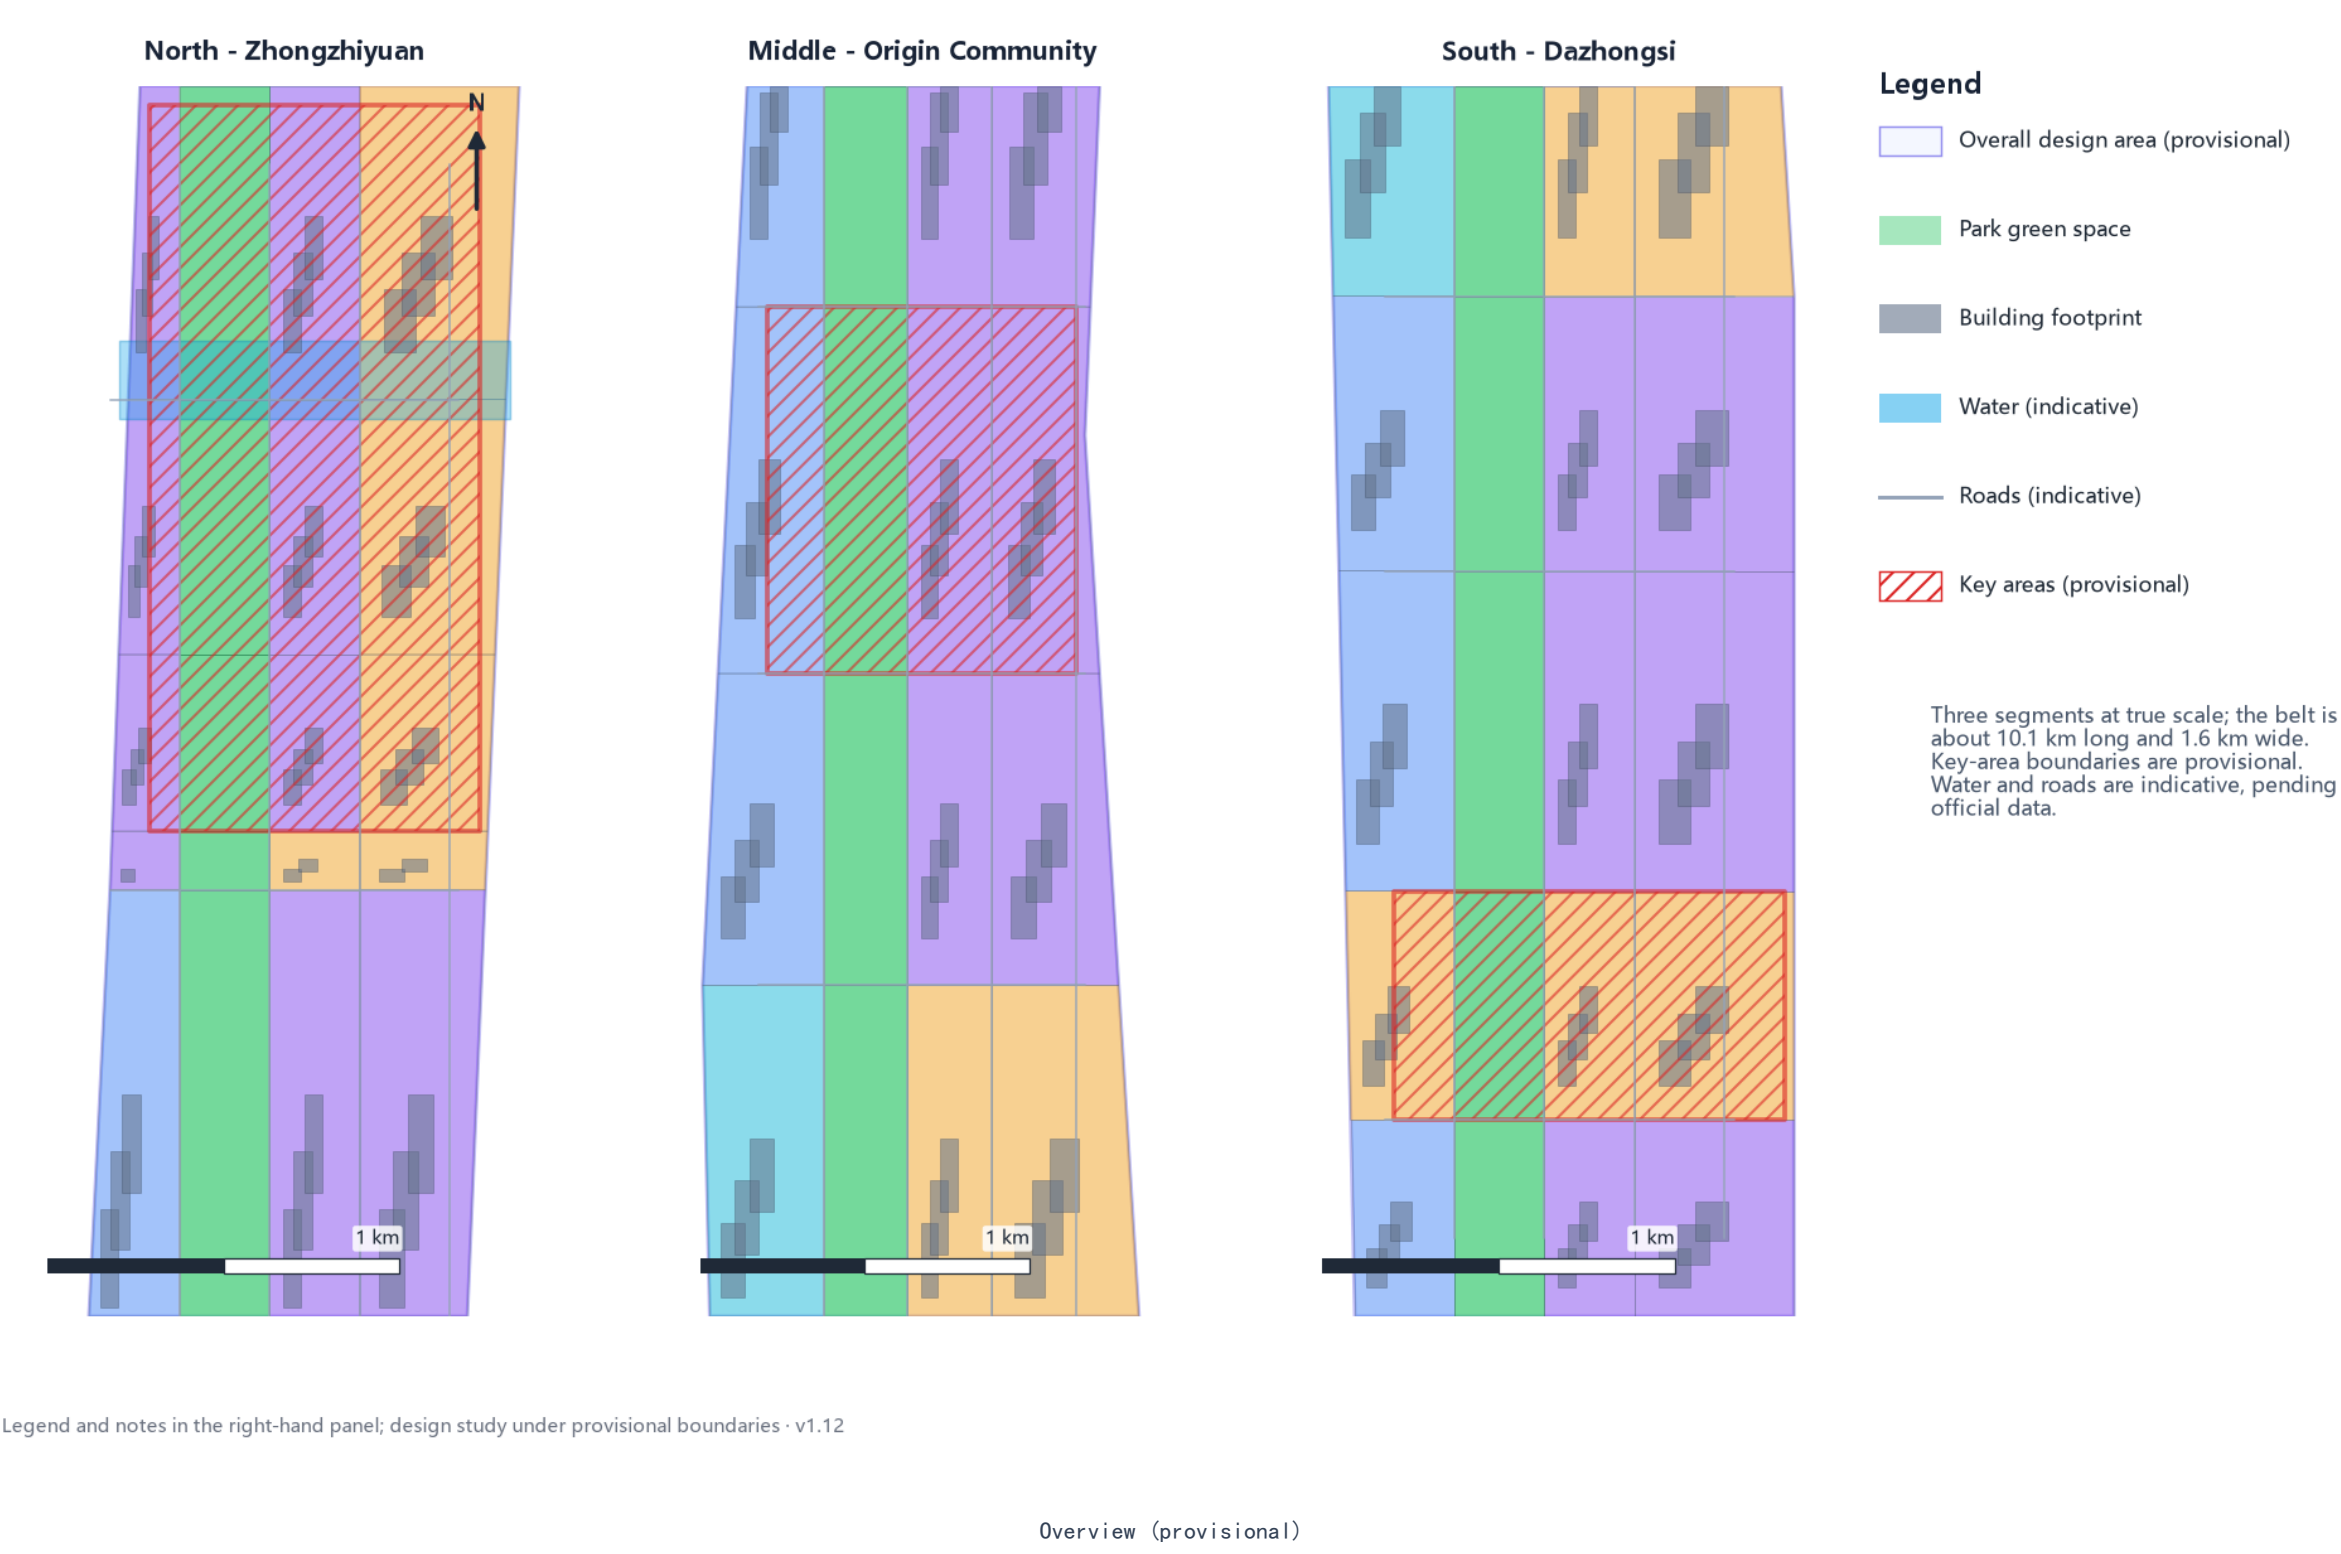

Location and Extent of the Three Key Areas (v1.12)

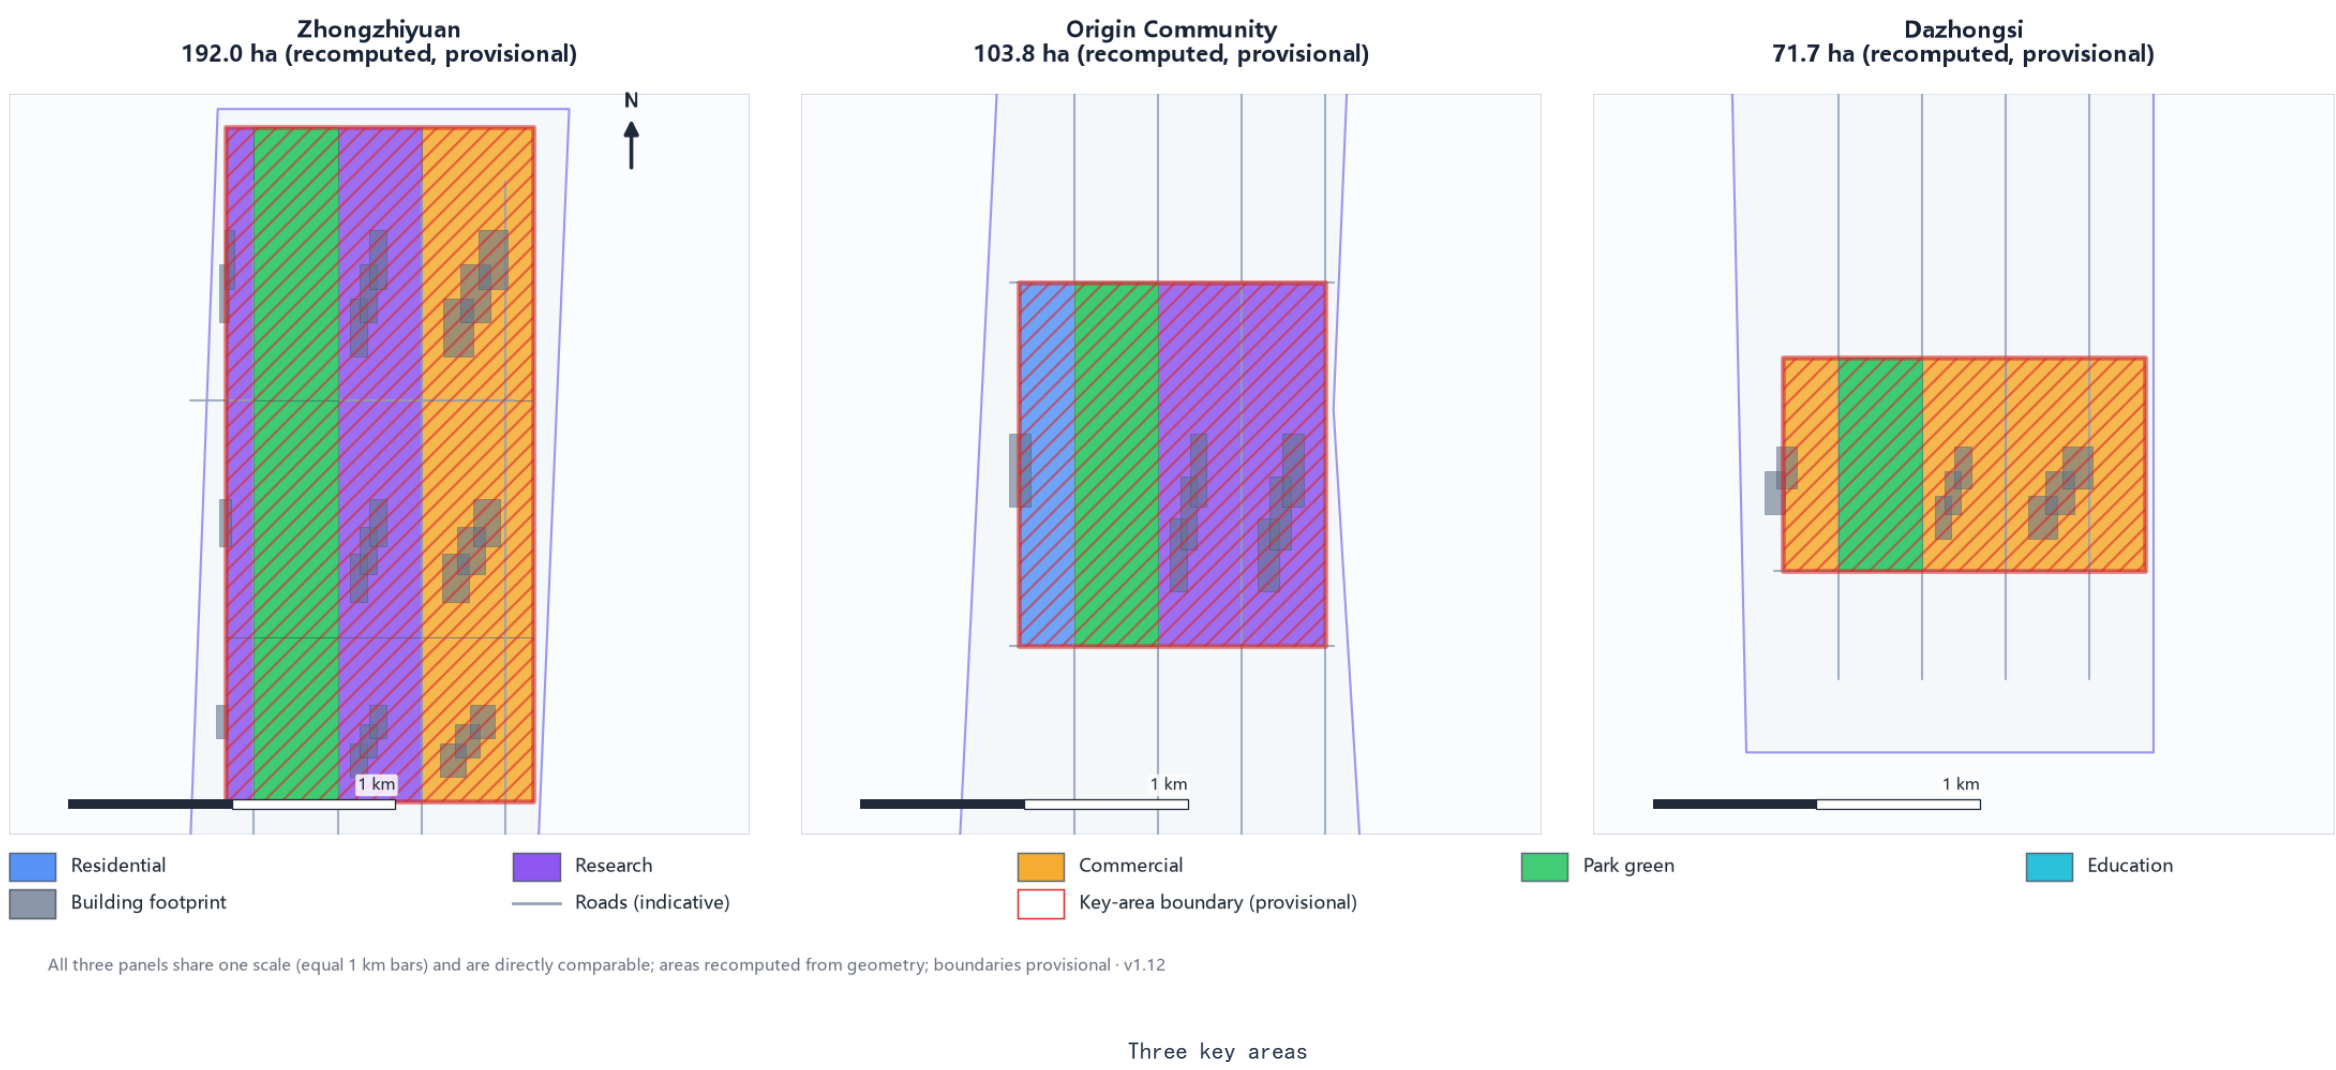


Land-Use Structure - Jing-Zhang Standing for People (v1.12)

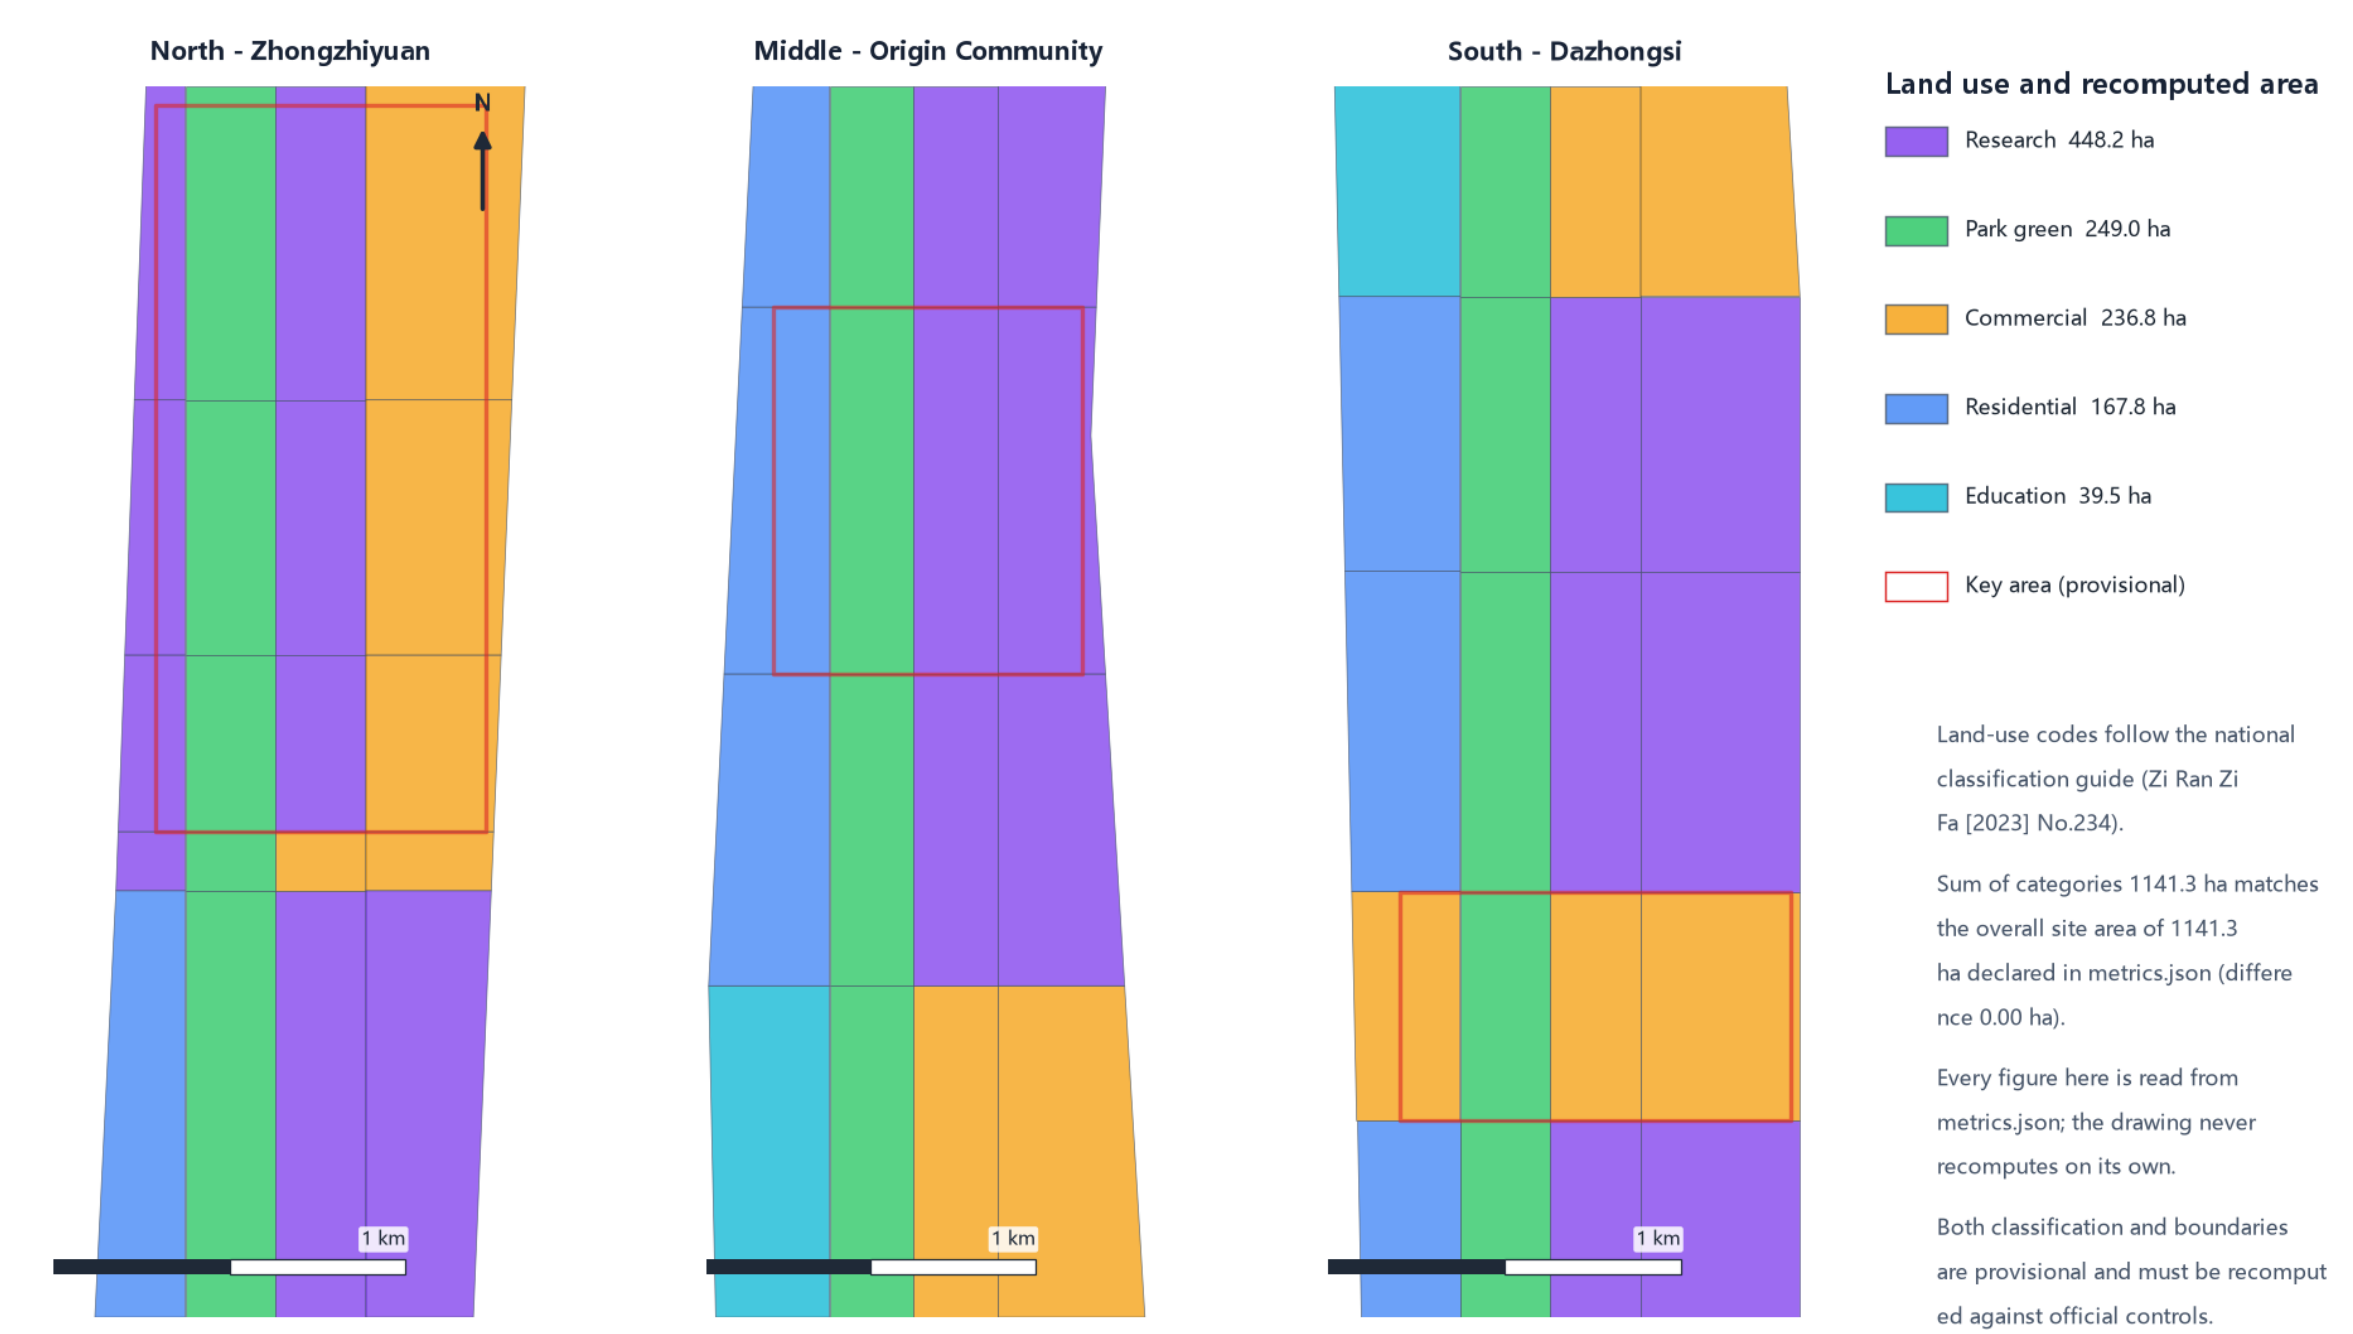

Areas recomputed from geometry; provisional boundary supports generation, discussion and revision only - v1.12

Land use


Transport, Slow Mobility and Blue-Green Public Space (v1.12)

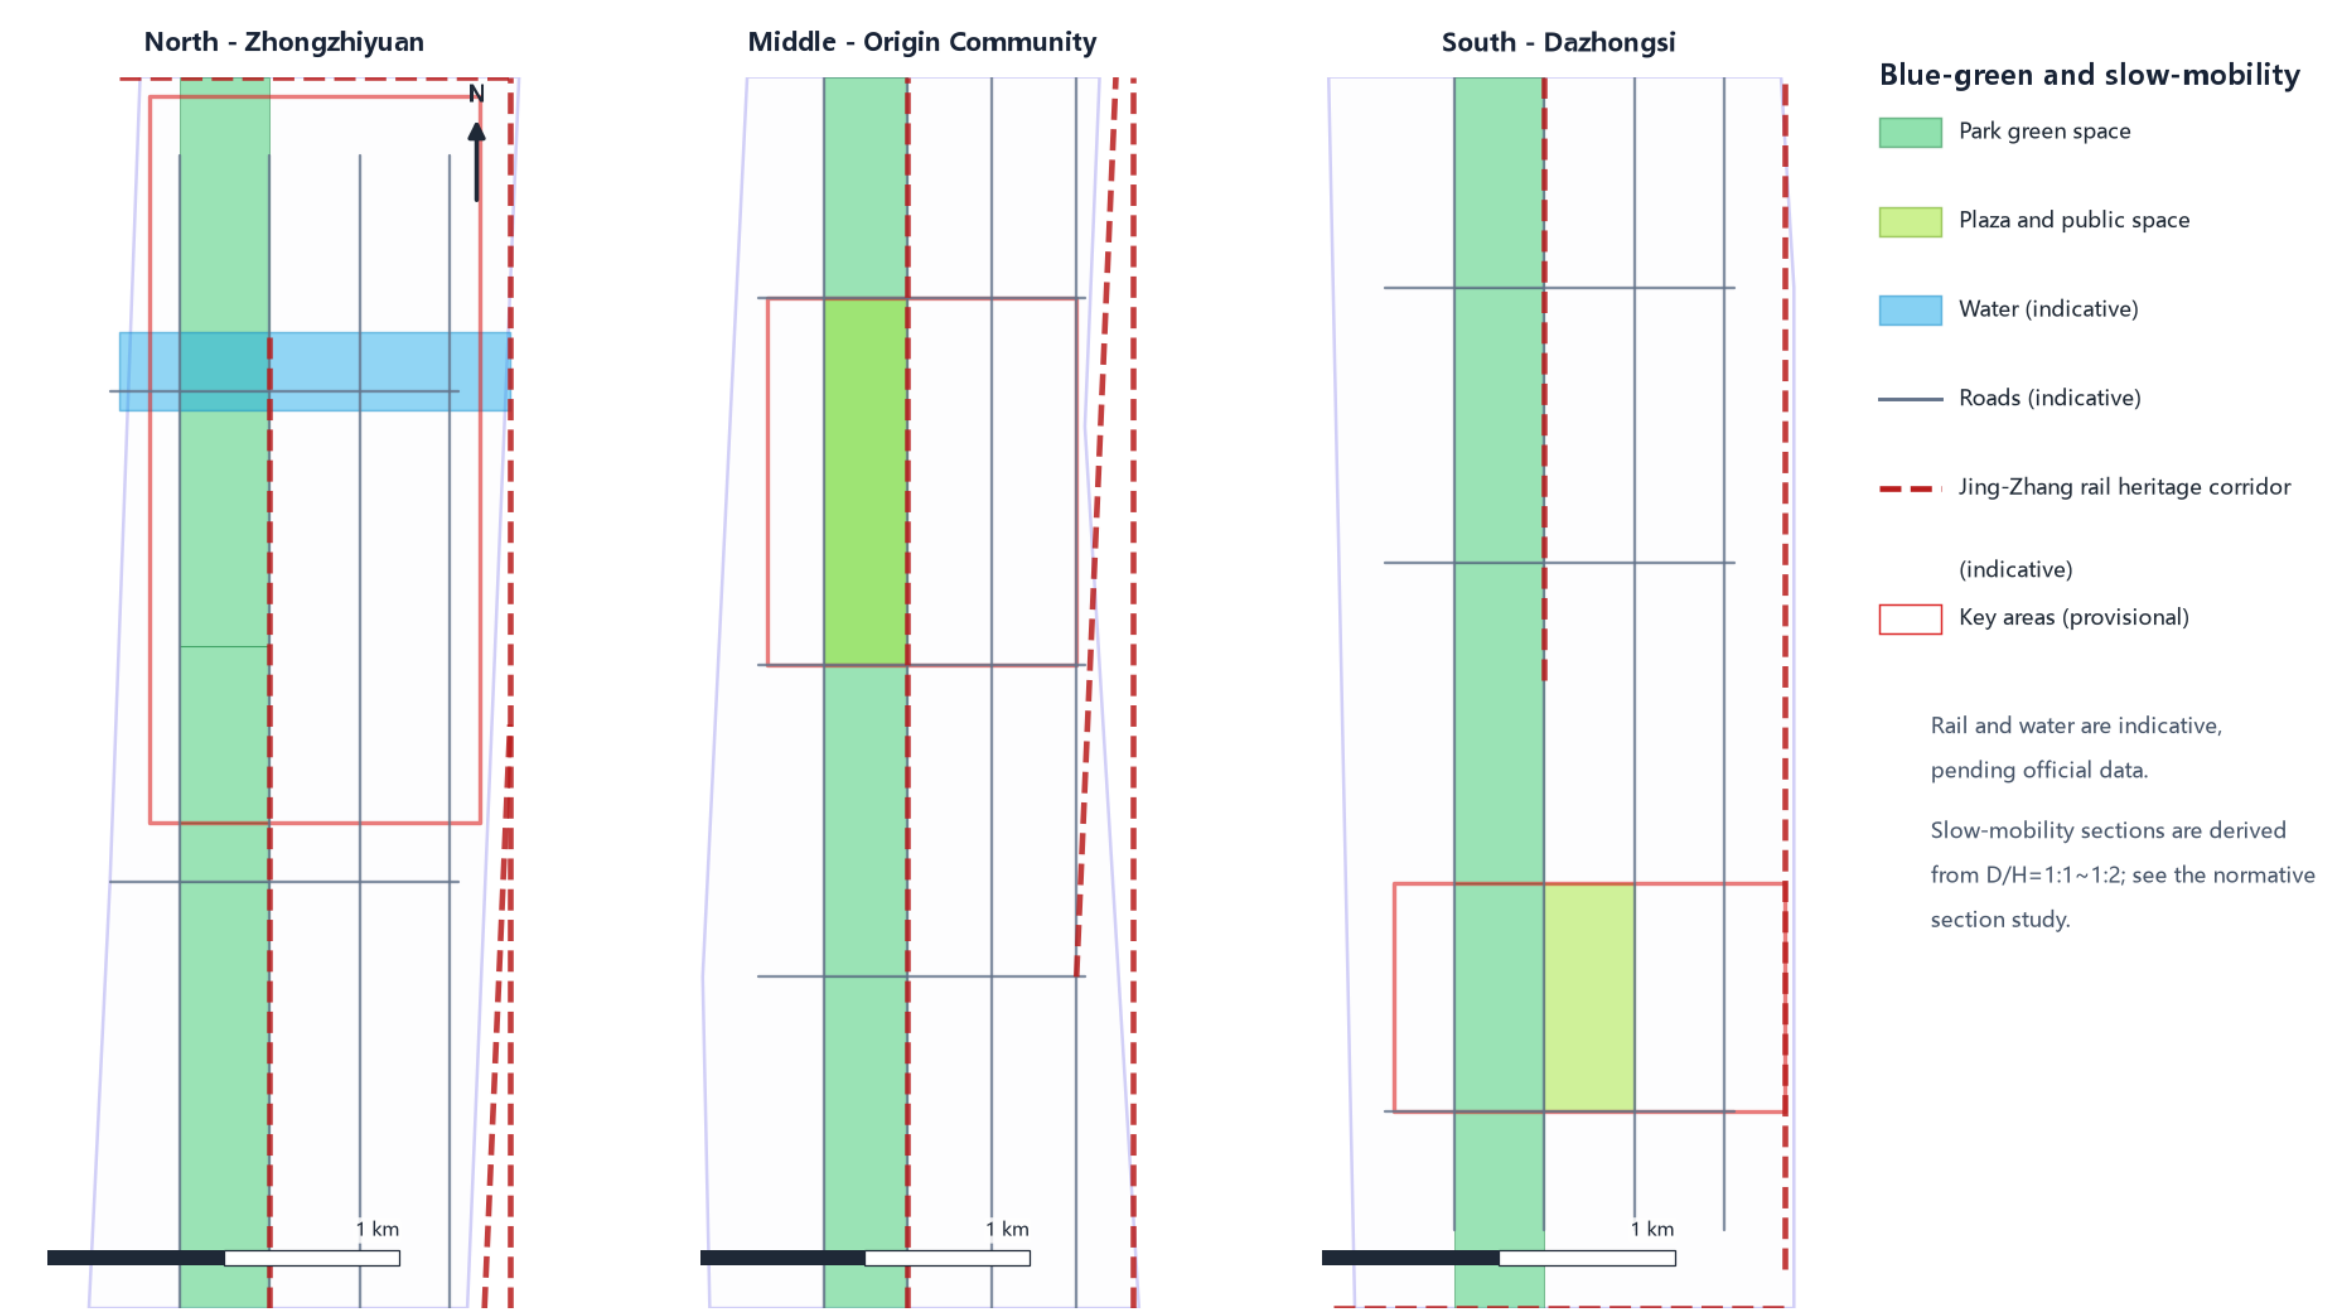

Water and rail indicative, pending official data - v1.12

Transport and blue-green

Physical Placement of the 12 AI Scenario Cards - One Belt, Three Cores (v1.12)

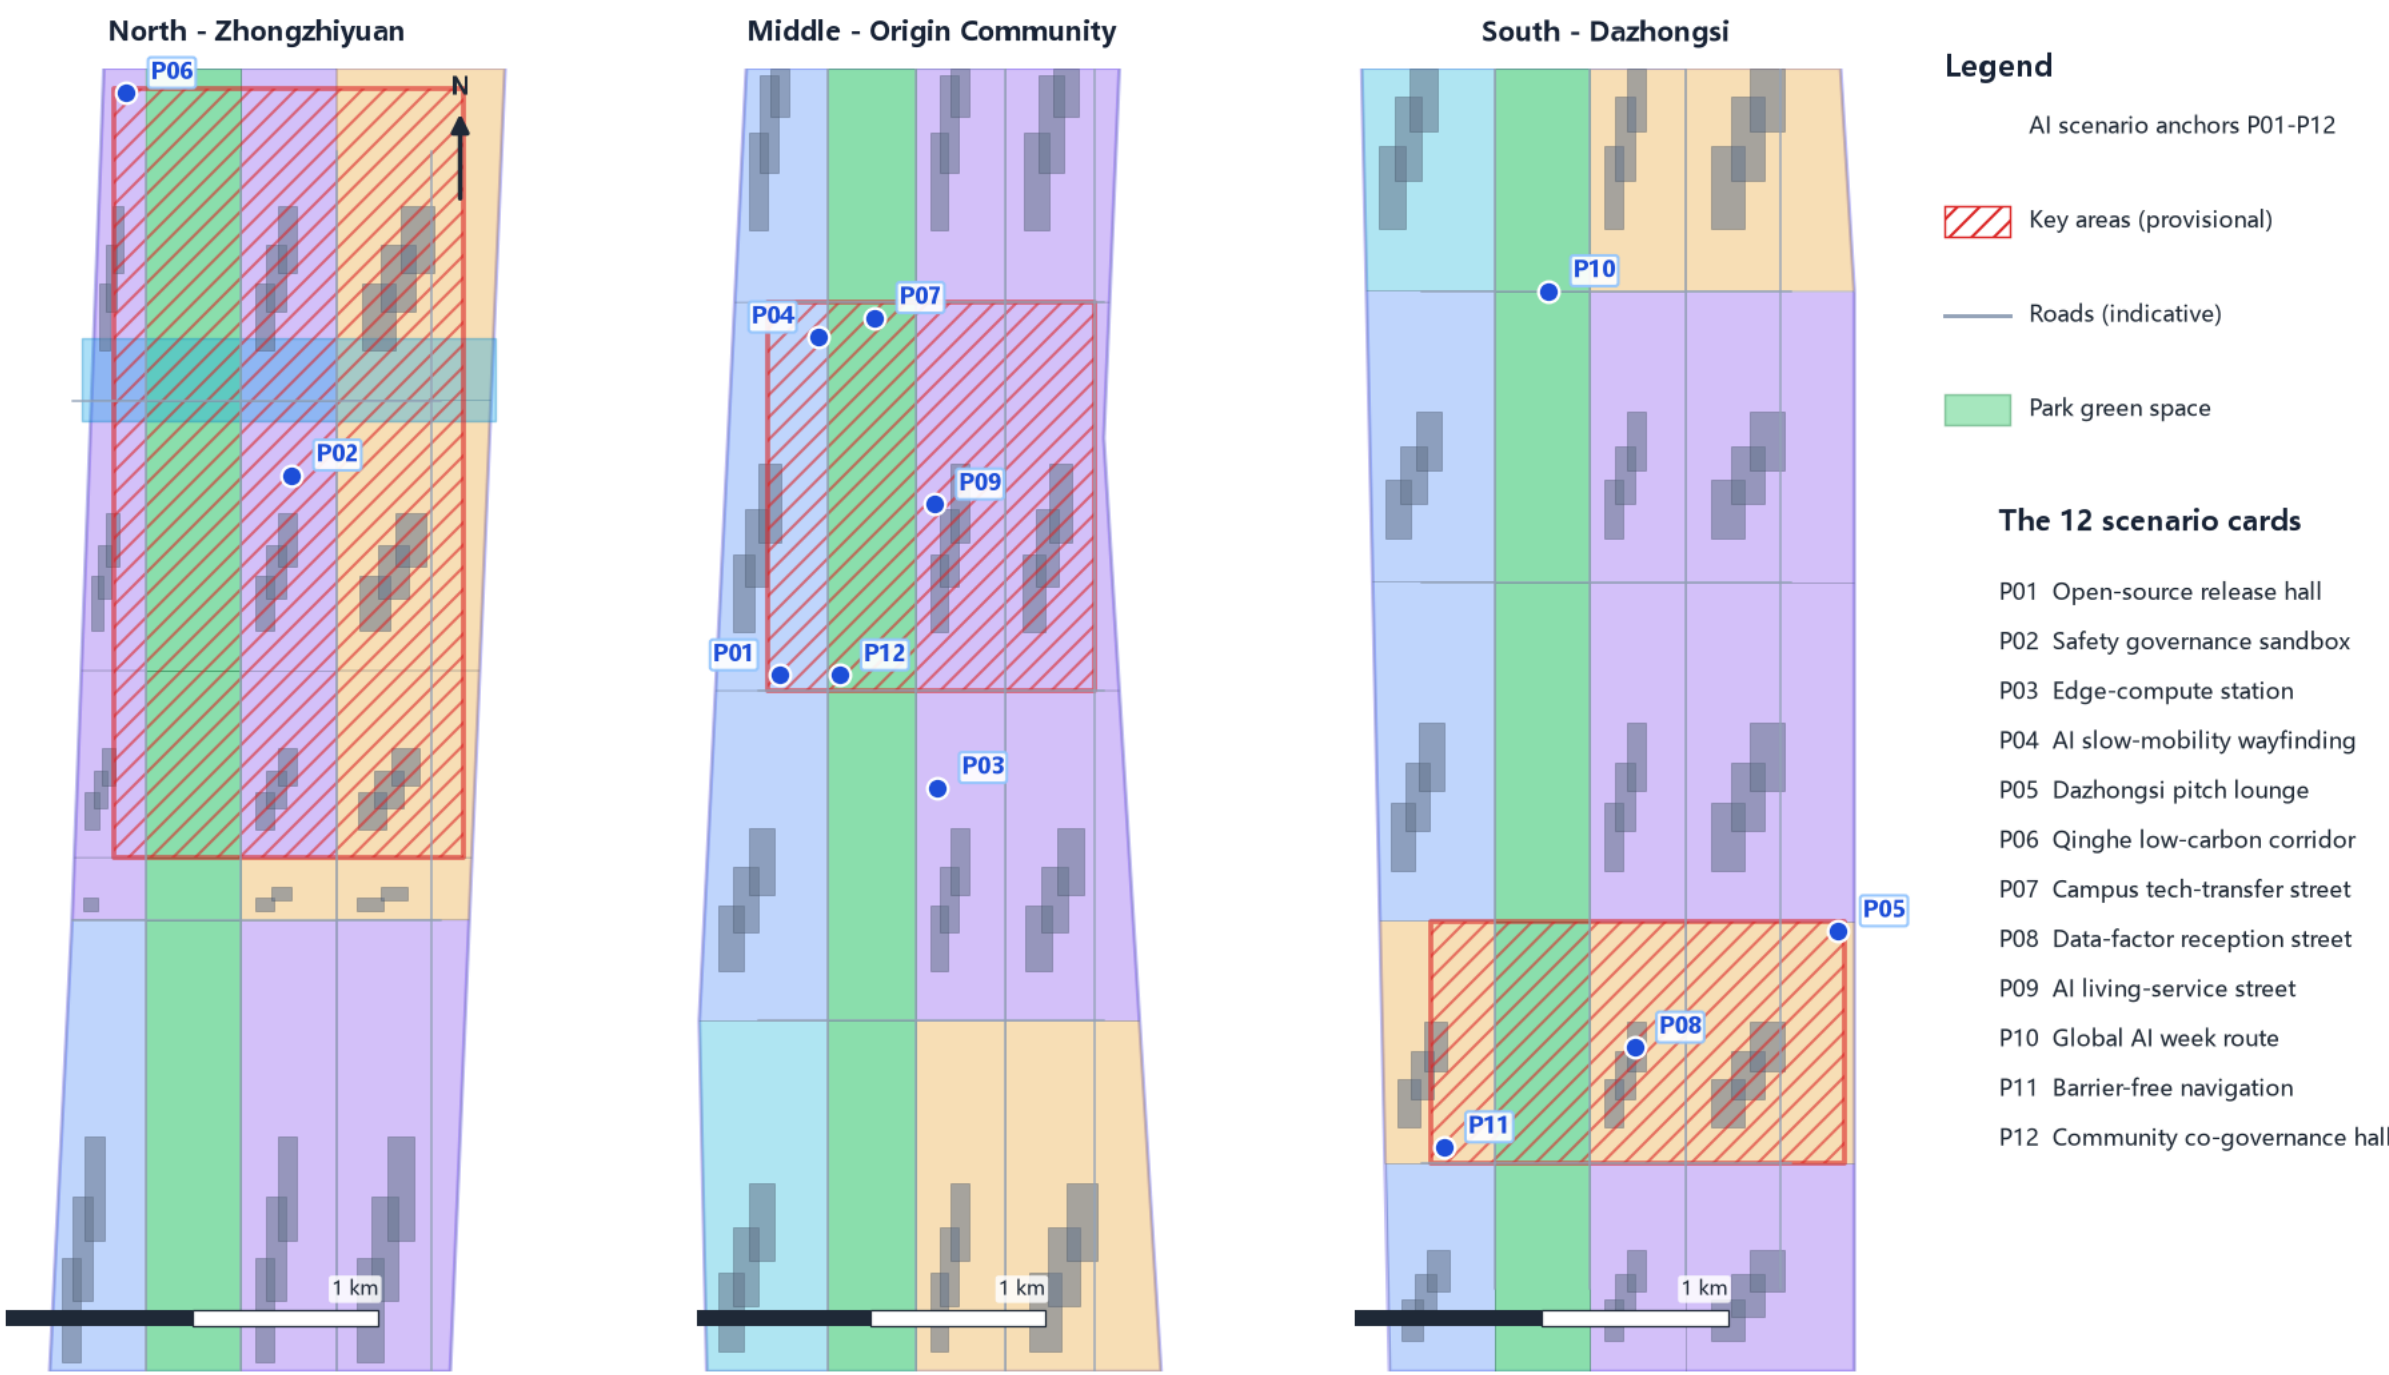

Card numbers map one-to-one onto anchors (card 01 -> P01 ... card 12 -> P12); placements are provisional pending site survey - v1.12

Fig 6 Physical placement of the 12 AI scenario cards


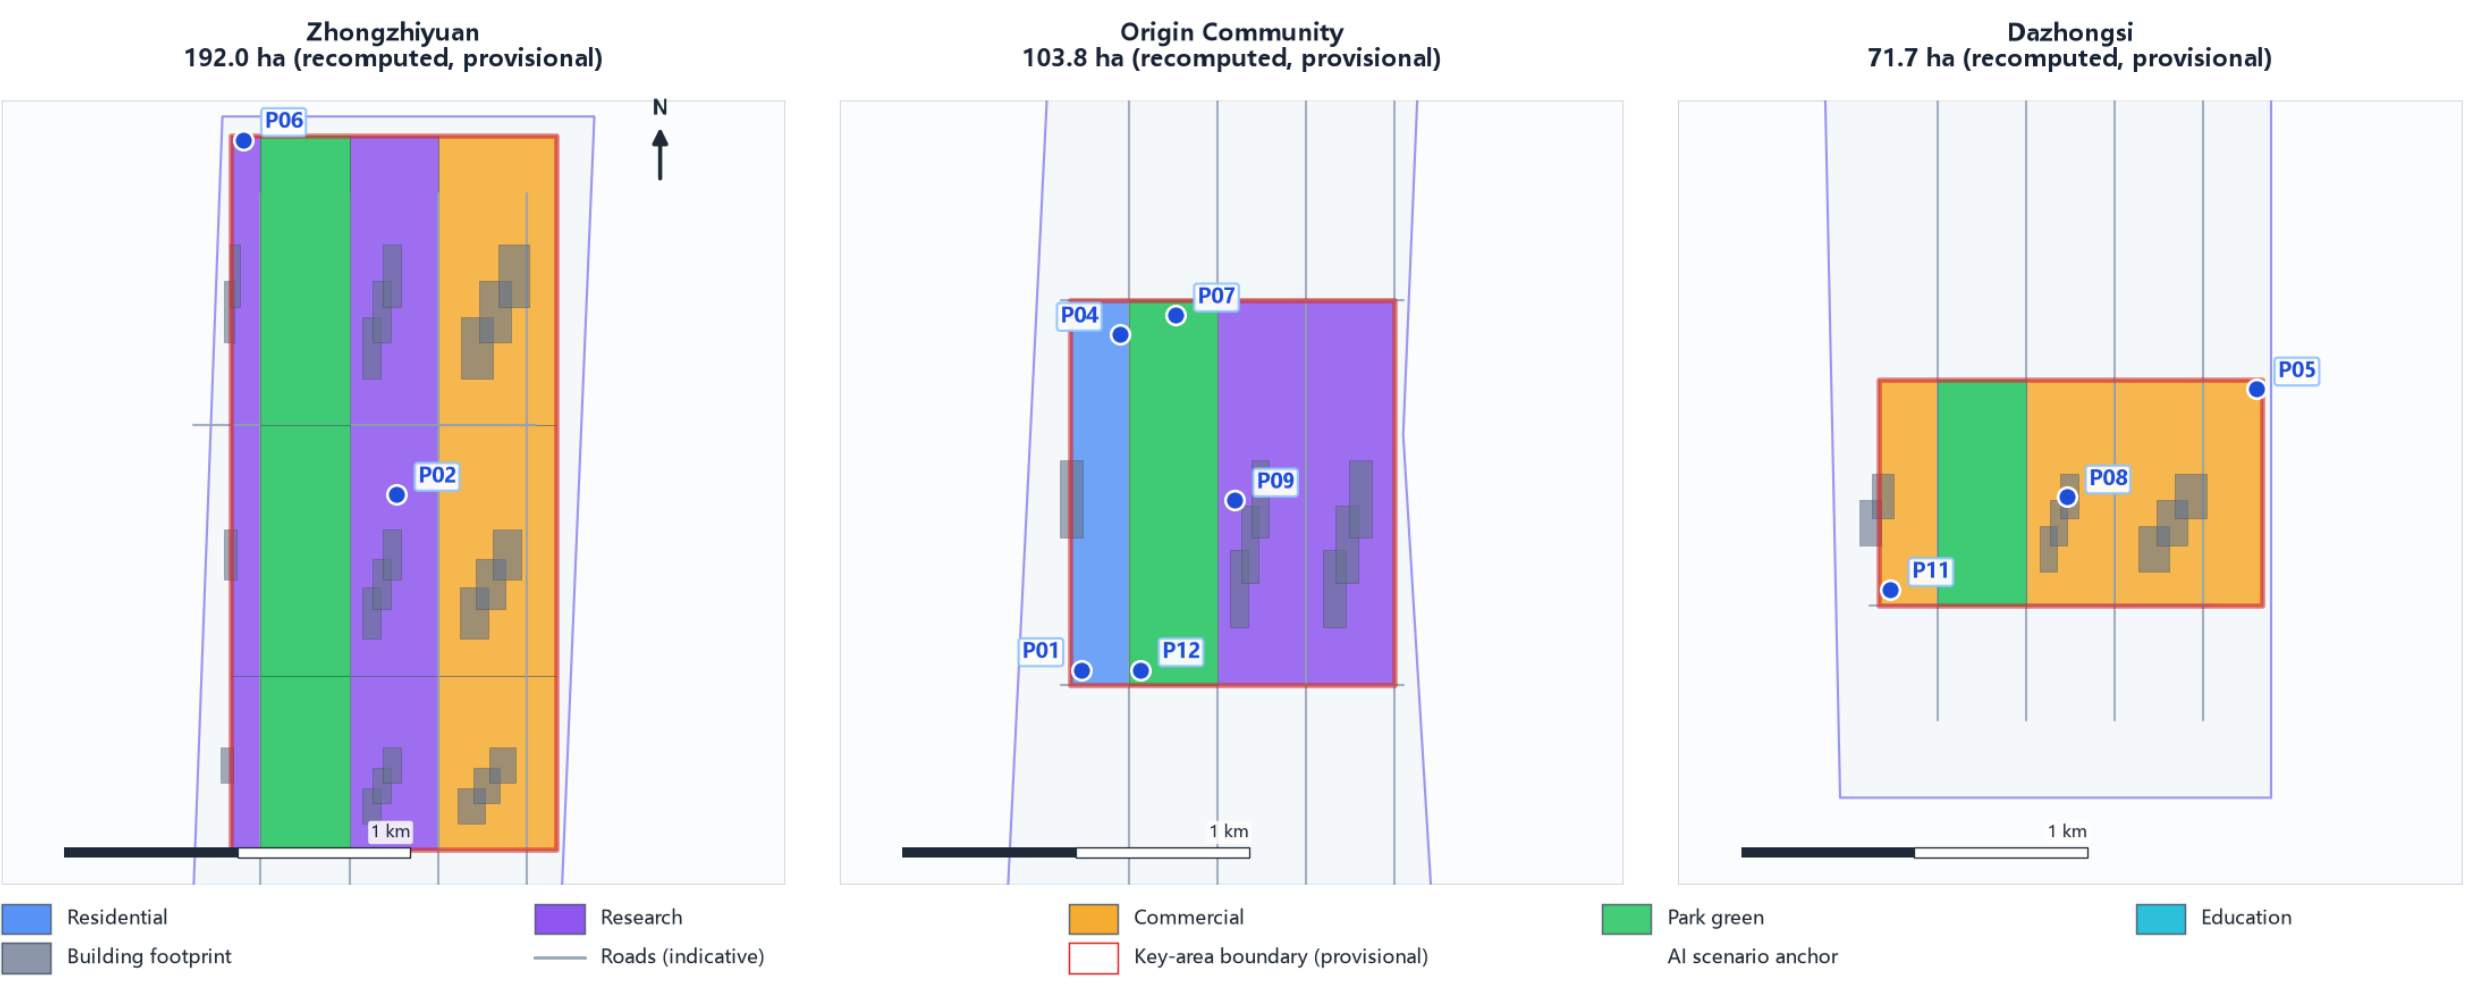


Fig 7 Site anchors and scenario placement in the key areas


Normative Street-Section Study - street width derived from the adopted D/H standard (not measured) (v1.12)

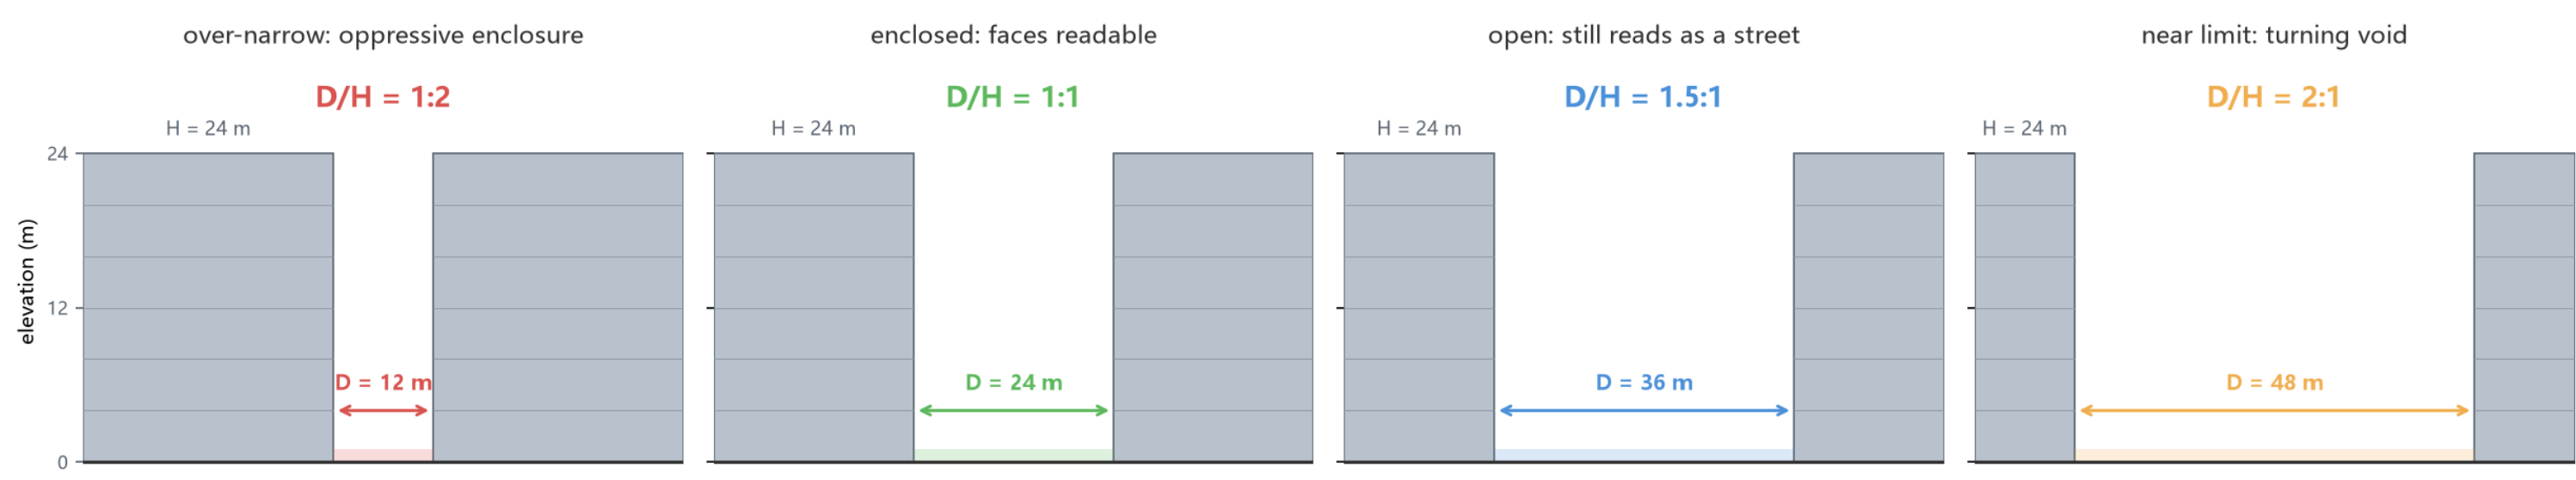

All four panels share the same building height (H=24 m) and the same scale; only the street width D changes.
H comes from the placeholder value in package geometry (all 104 footprints at 24 m / 6 storeys; no variation) and the road layer carries no width field;
so this is not an as-built survey but a normative judgement, from Ashihara Yoshinori: The Aesthetics of the Street (D/H=1:1-1:2)
and Jan Gehl, Life Between Buildings (20-25 m social distance ceiling). Redraw once official controls and surveyed sections exist.

Fig 8 Normative sections: widths derived from D/H=1:1-1:2 and the 20-25 m social distance; building height uses the placeholder 24 m in package geometry, not a surveyed cross-section

Core Metrics Recalculated and Evidence Chain (v1.12)

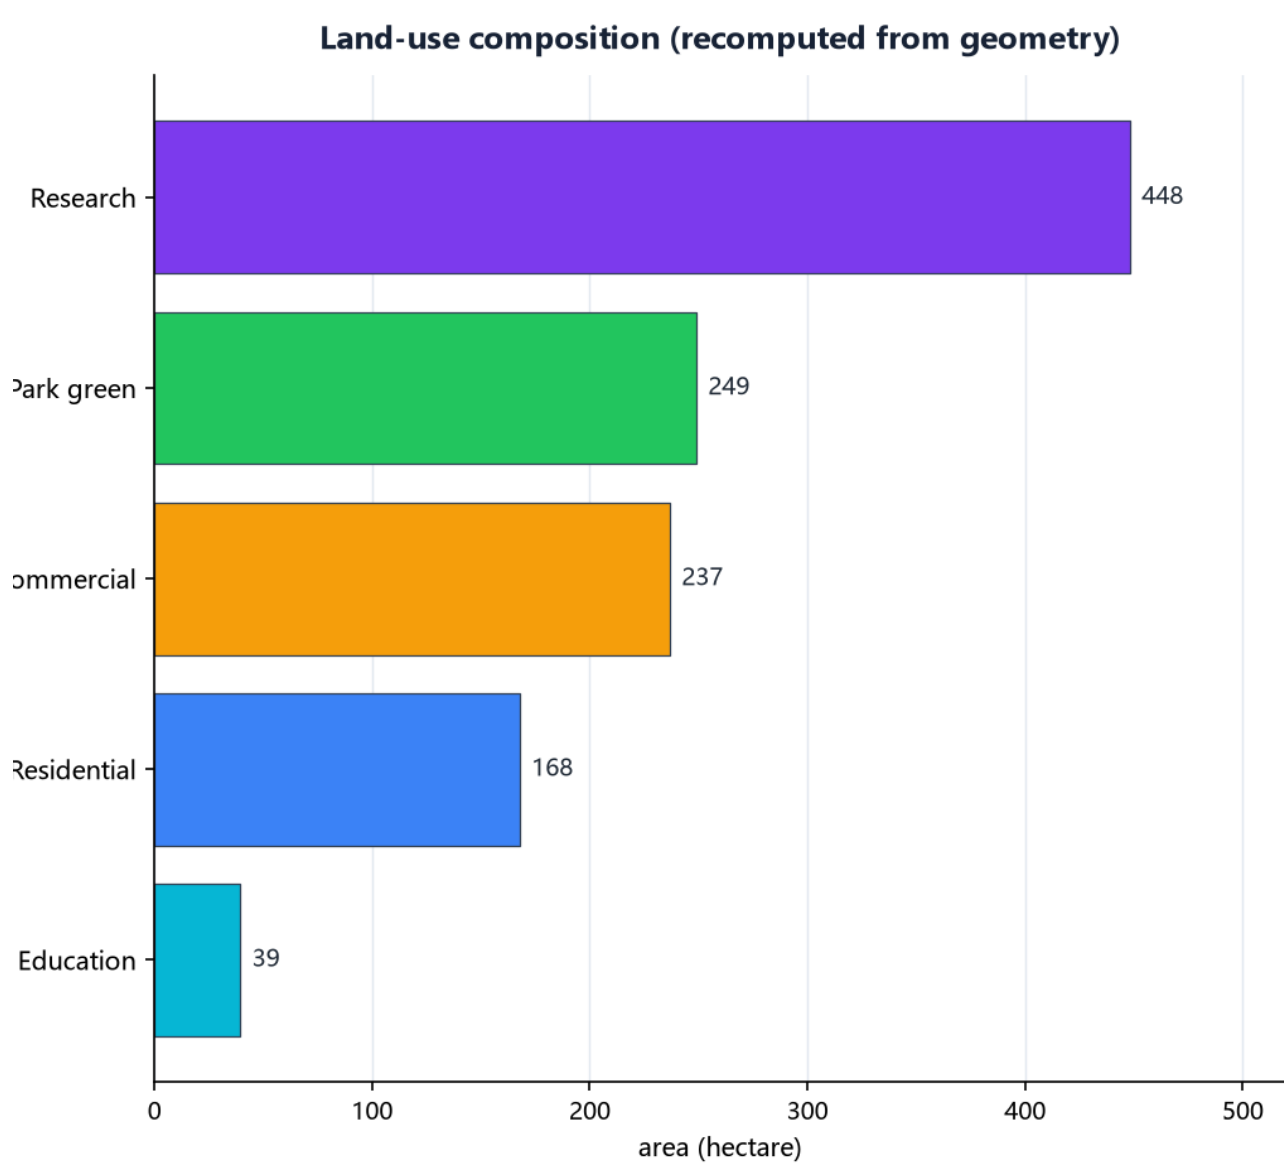

All metrics recomputed from package geometry; provisional boundary supports generation, discussion and revision only - v1.12

Core metrics and evidence status

Overall site area	1141.3 ha	known
Green ratio	21.8%	known
Public space ratio	3.9%	known
Building footprint	97.8 ha	known
Number of key areas	3	known
Floor area ratio	no basis - pending official data	unknown
At-off service coverage	no basis - pending field observation	unknown
Failure-sample reporting ratio	no basis - pending field observation	unknown
Pilot-readiness fields	8	known
Ledger cells verifiable in package	12/96 = 0.125	known
Frozen ledger cells (no numbers)	24	known

The three unknowns are deliberately left without numbers: with no public baseline the field and its responsibility are frozen; estimates may not pass as measurements.

provisional boundary - for display and discussion only

Core metrics (provisional)